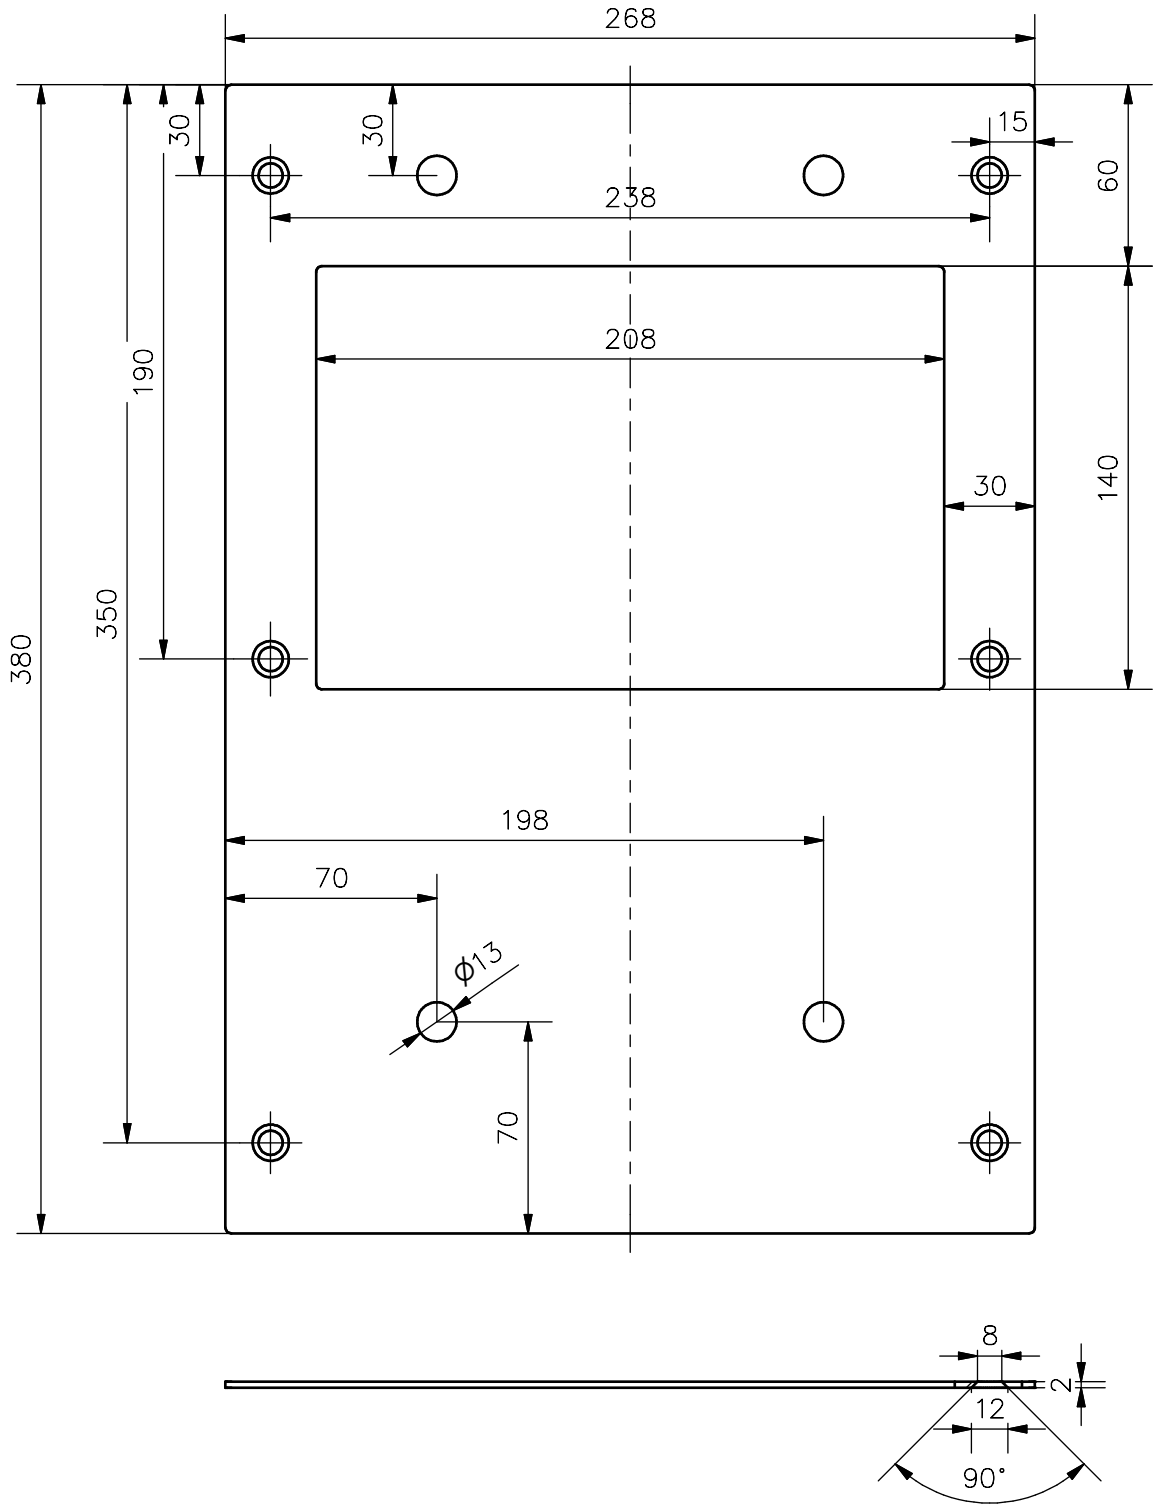


ELEMENTO	CTDAD	Nº DE PIEZA	DESCRIPCIÓN	MASA
1	1	base	base acero	1,126 kg

	NOMBRE	FECHA	FIRMA
Dibujado	Juanjo Rodríguez	22/05/2020	
Comprobado	Víctor Esteve		

Sant Jaume Apòstol
Col·legi Parroquial

ESCALA	CONJUNTO:	Nº de plano
1:2,5	Cabrestante	1
	PLANO: base	